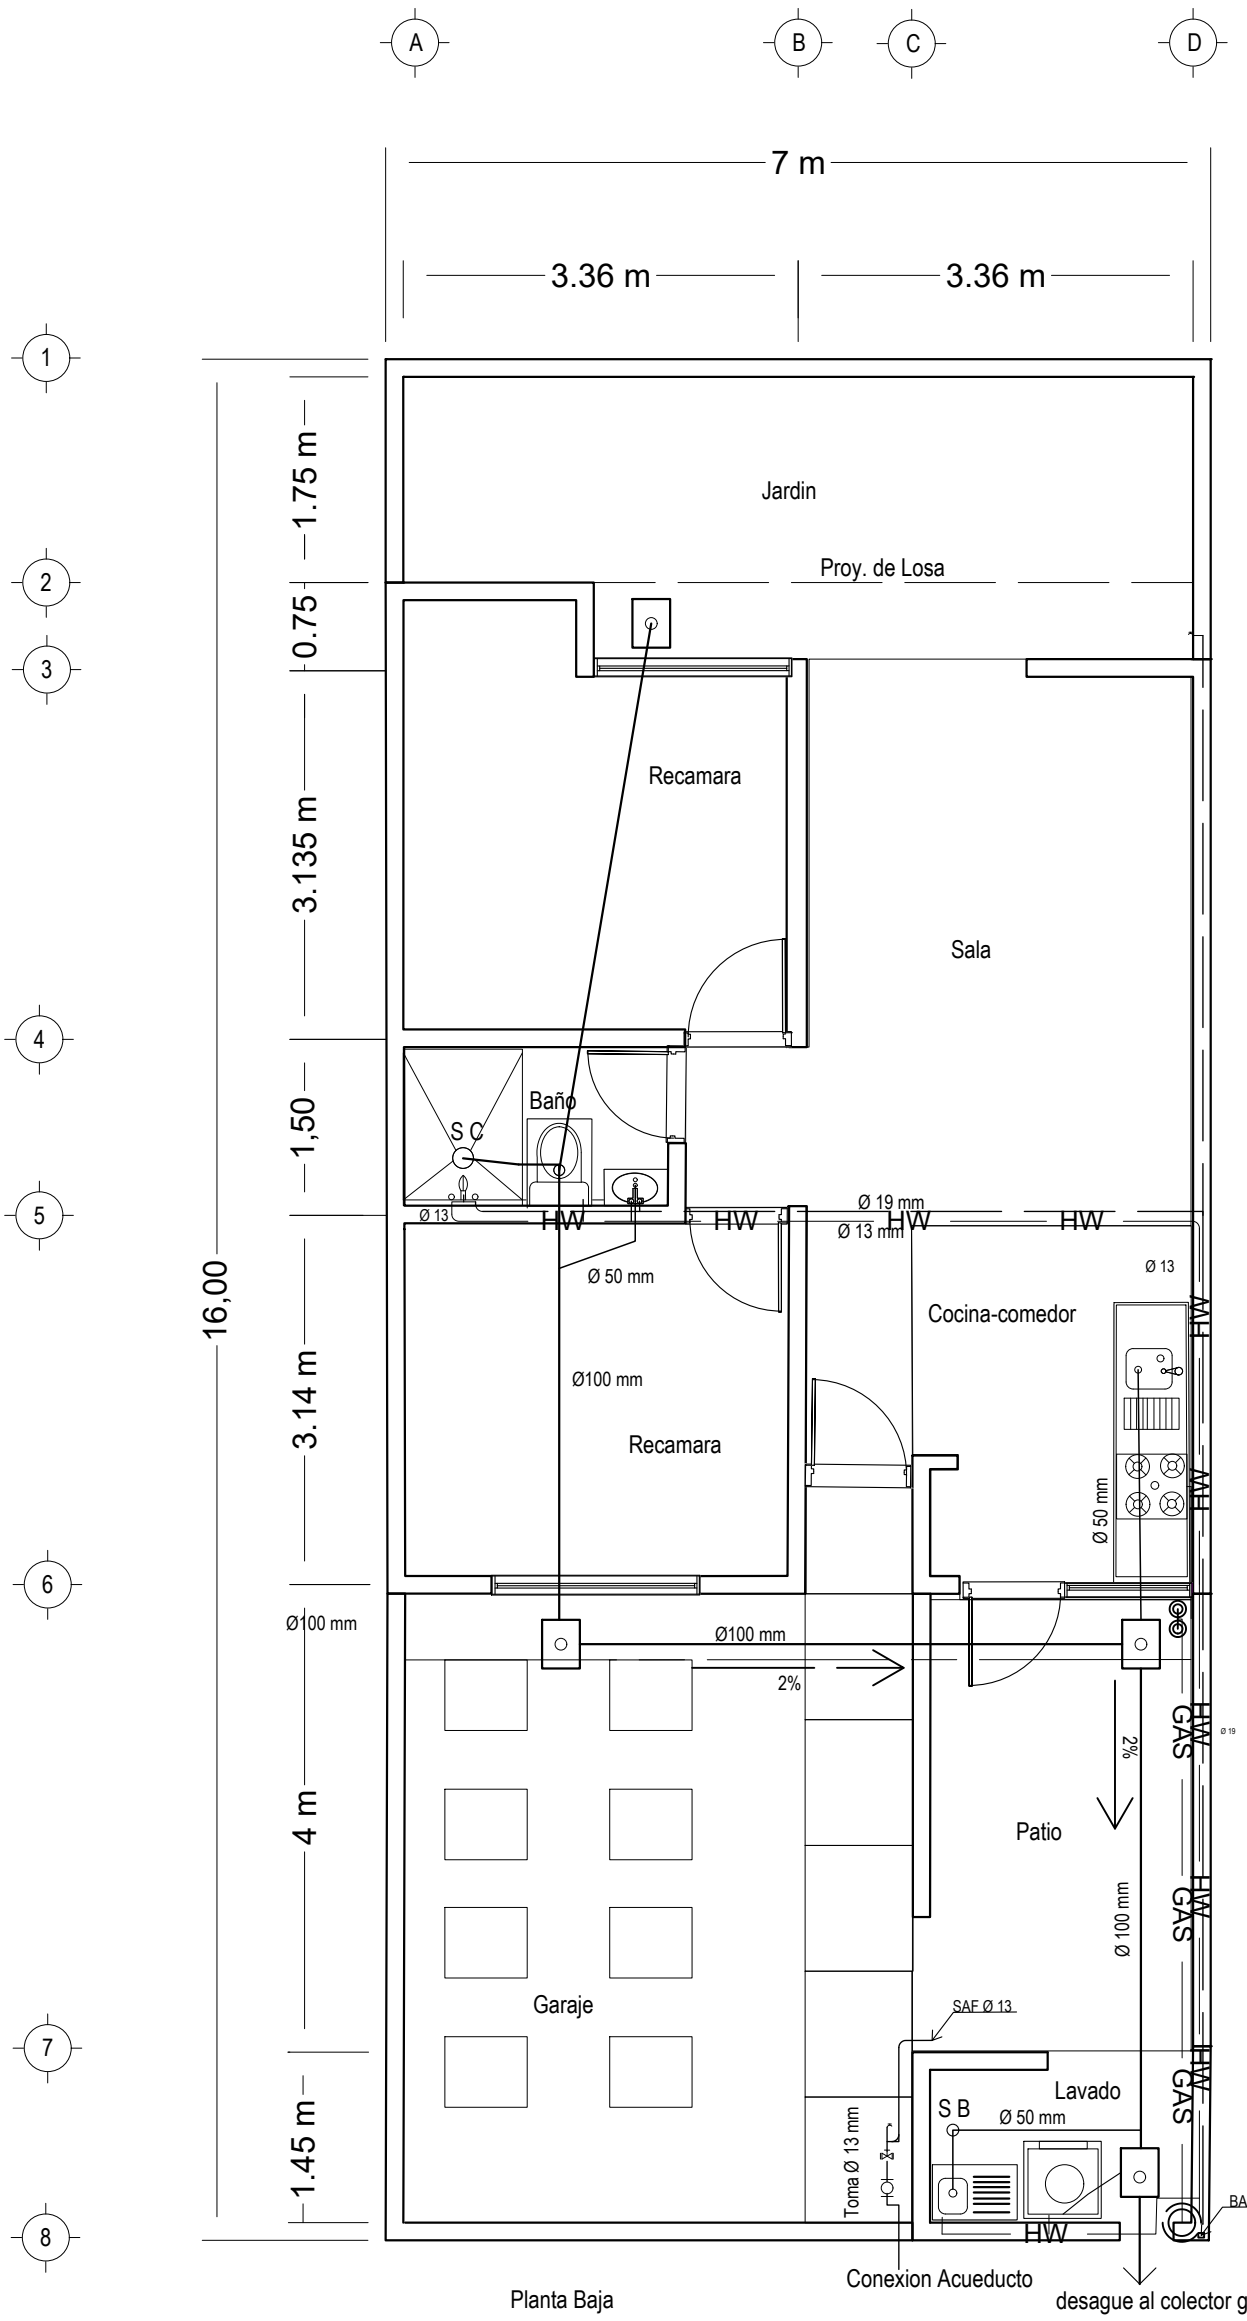

Simbología hidrosanitaria y de gas	
BAF	Bajada de agua fría
SAF	Subida de agua fria
S B	sifón de bote
S C	Sifón de coladera
	LLave de jardin
	Registro sanitario
	Medidor de agua
	Válvula de control
	Tanques de gas
	calentador
HW	Agua caliente cobre tipo "M"
	Agua fria cobre tipo "M"
GAS	Tubería de gas
	Tubo de PVC de 50mm y 100mm

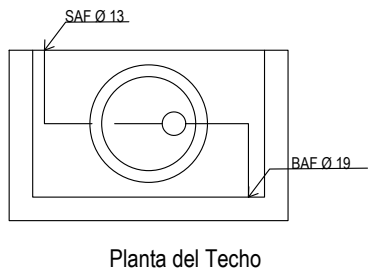

IBG Ingeniería Lukas I Bustos G. Ingeniero Ambiental	Notas: Basado en el libro plano casa Agustin Ceballos	Dibujó: Ing. Lukas I Bustos Granados	Proyecto: Casa tradicional	Código: AA-02
		Reviso: Ing. Lukas I Bustos Granados	Título: Plano hidrosanitario y gas	Escala: 1:100 Fecha: 04/09/2024